



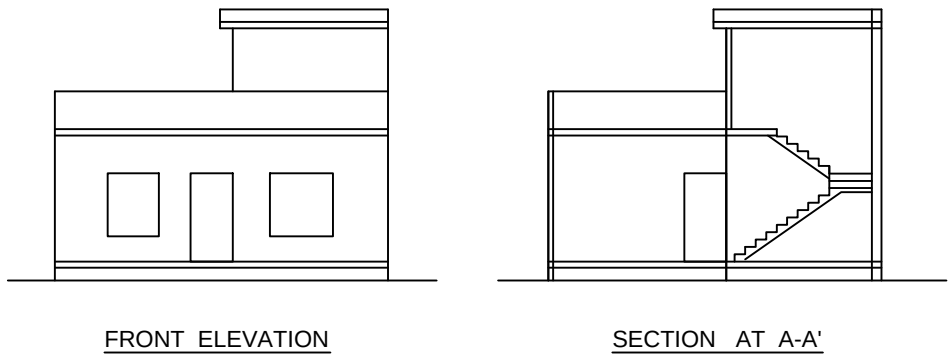


FRONT ELEVATION


SECTION AT A-A'

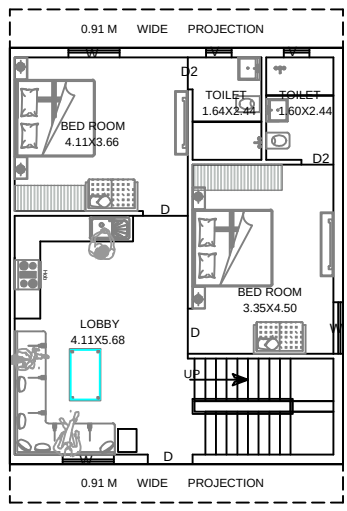



GROUND FLOOR PLAN

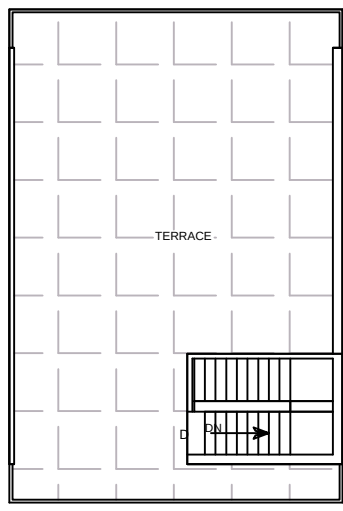


TERRACE FLOOR PLAN

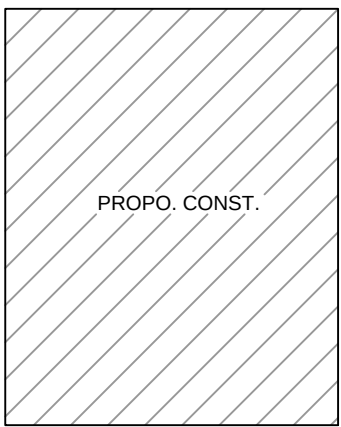


SITE PLAN

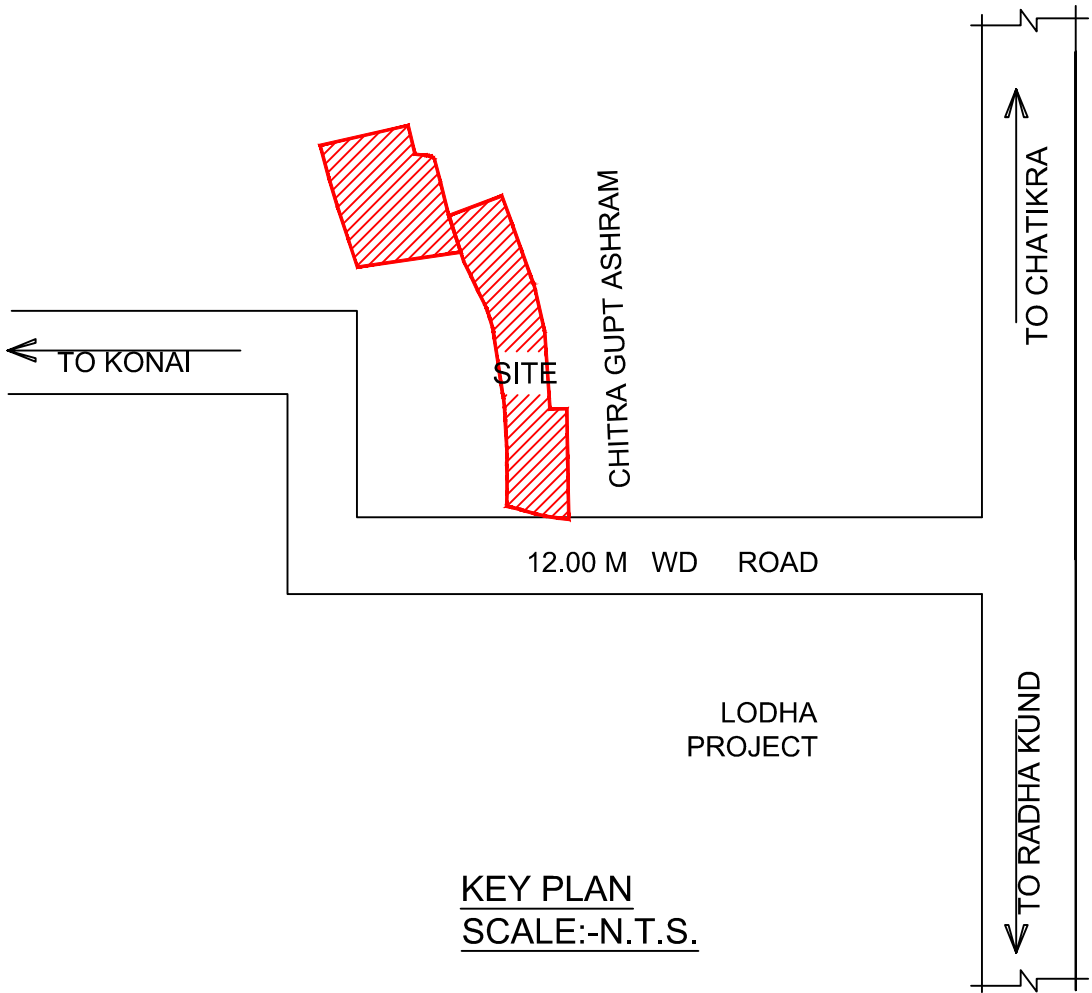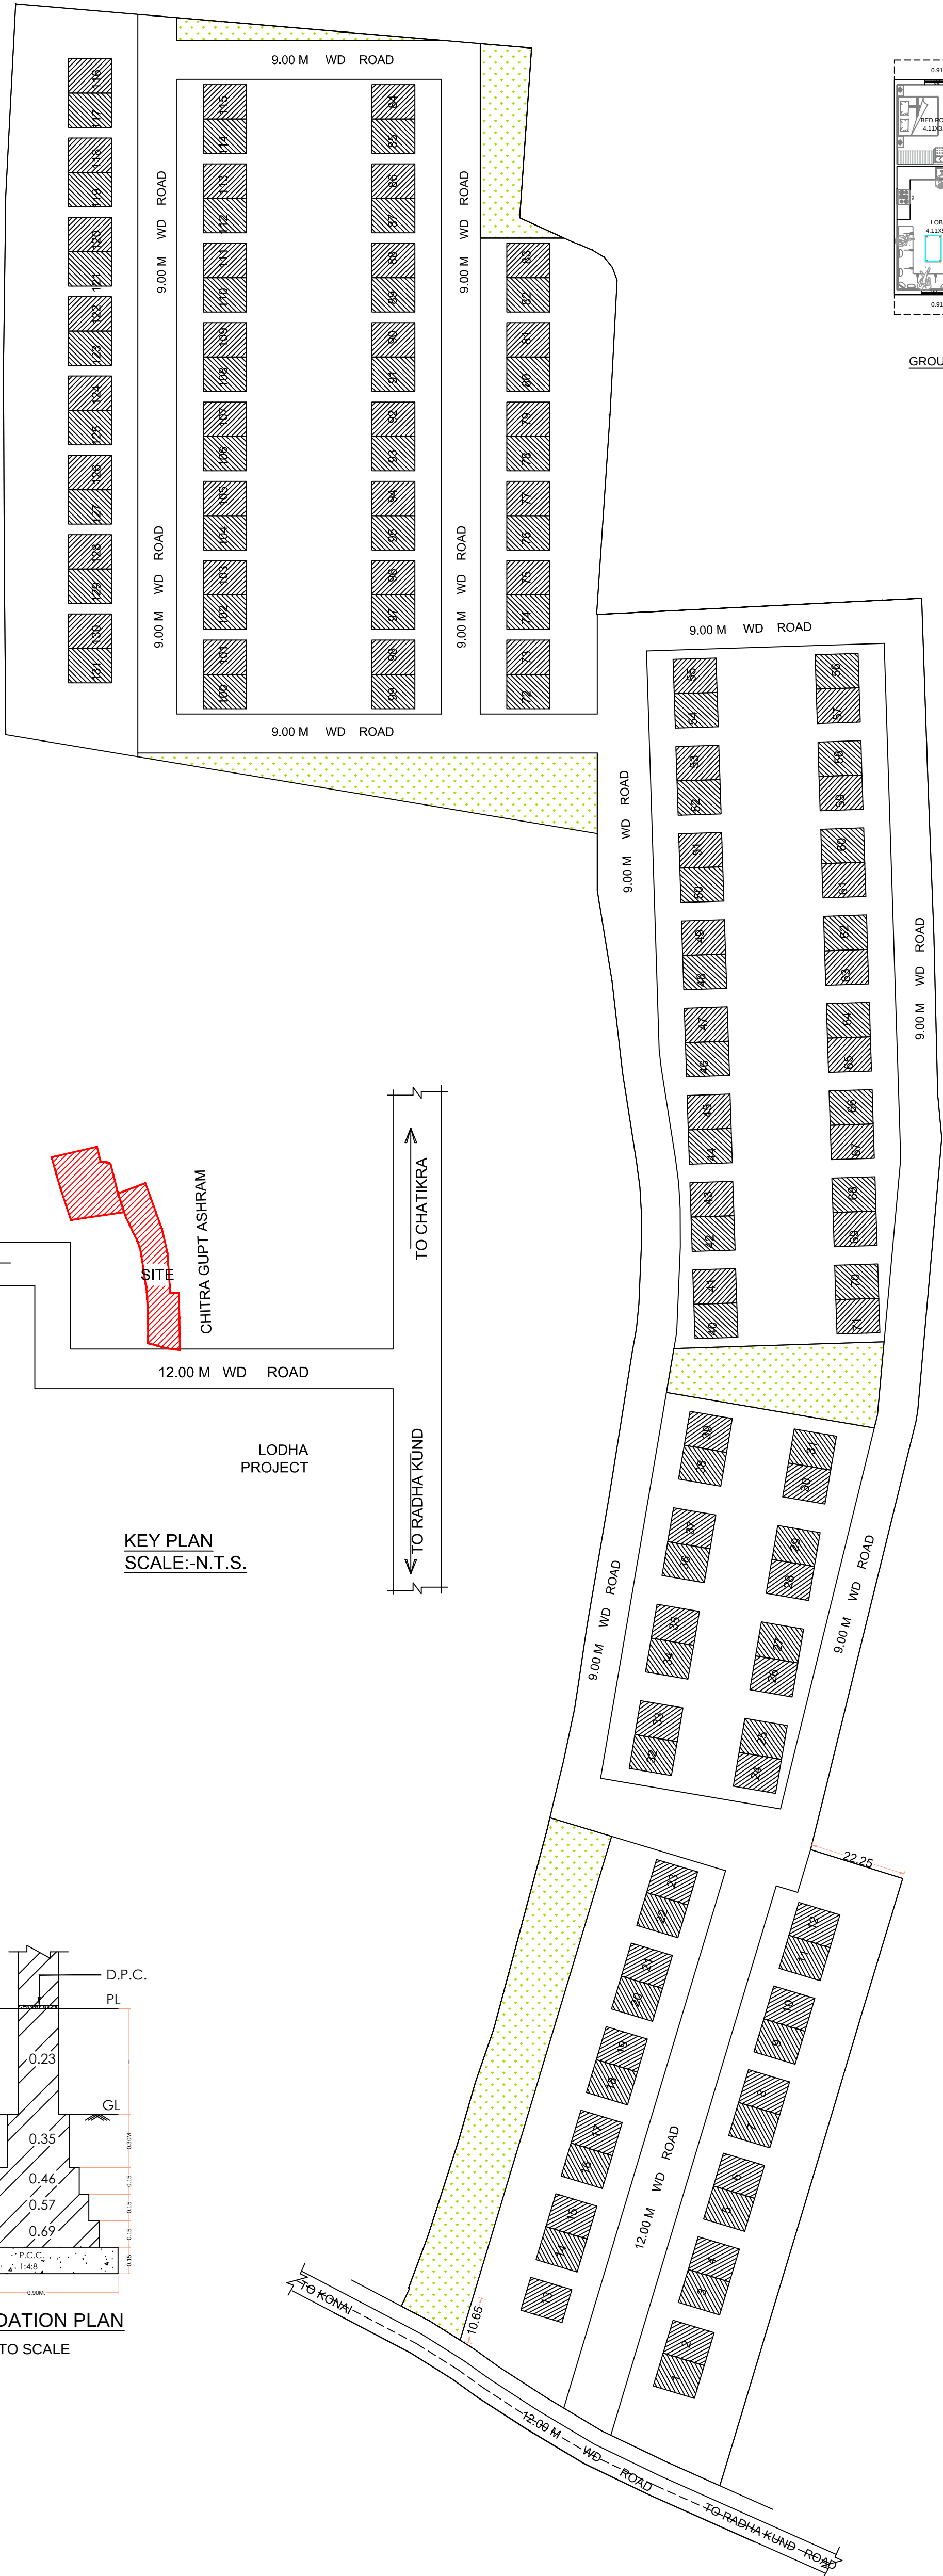


KEY PLAN
SCALE:-N.T.S.

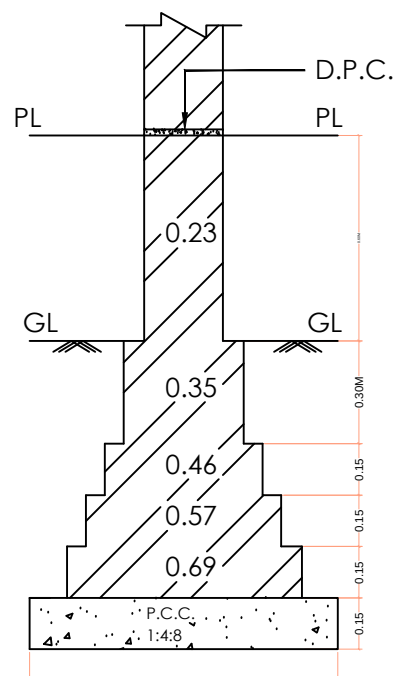

FOUNDATION PLAN
NOT TO SCALE

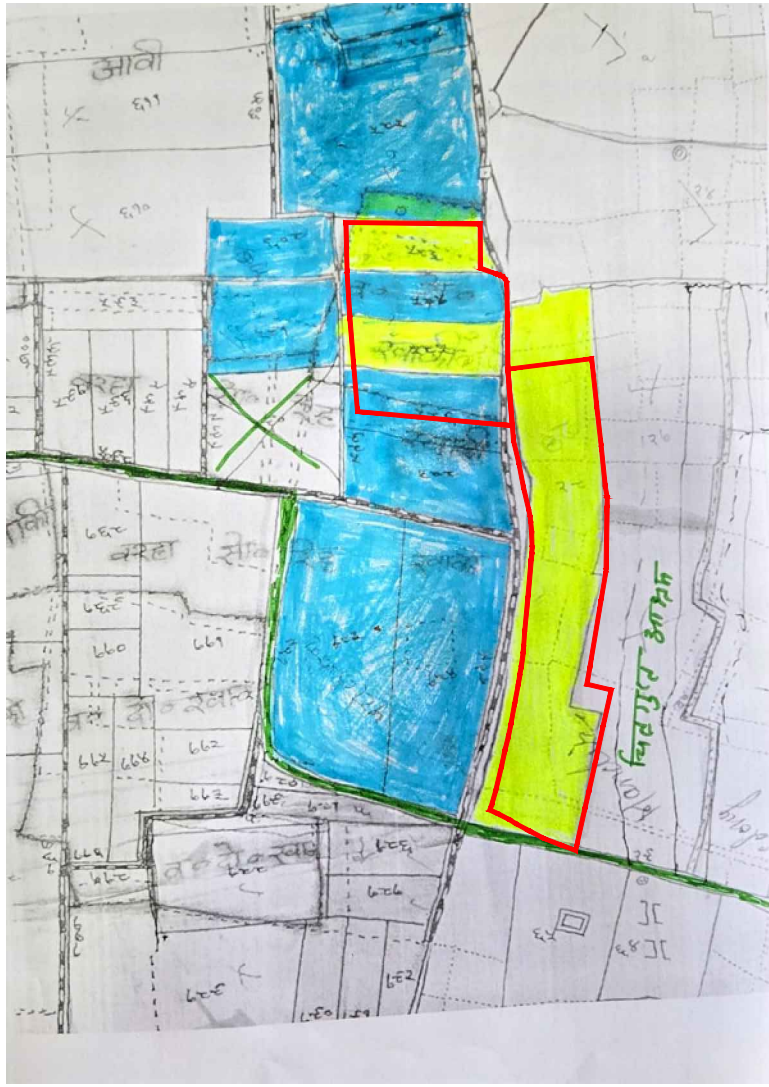

SAJRA PLAN

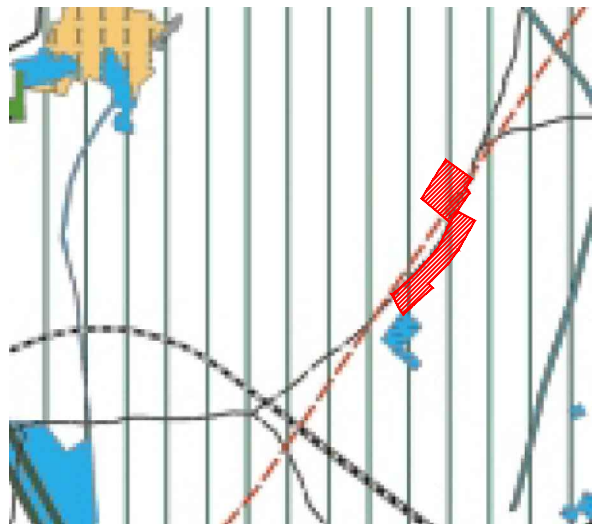

MASTER PLAN



GOOGLE IMAGE PLAN

SPECIFICATION :-

- 1- 1:4:8 P.C.C. IN FOUNDATION
- 2- 1:2:4 R.C.C. IN SLAB , BEAM & LINTEL .
- 3- 1st CLASS BRICK WORK IN FOUNDATION AND SUPAR STRUCTURE.
4. 12MM THICK PLASTER IN (1:6) CEMENT SAND MORTAR.
- 5- SAL WOOD CHAUKHATES AND SHEESHAM WOOD DOOR .
- 6- MARBLE CHIPS FLOORING.

SCHEDULE :-

DOOR	D1	-	1.00 M X 2.10 M
	D2	-	0.90 M X 2.10 M
	D3	-	0.75 M X 2.10 M
WINDOW	W	-	1.20 M X 1.20 M
	W1	-	1.80 M X 1.80 M
VENTILATER	V	-	0.60 M X 1.05 M

AREA CHART :-

	AREA (SQM)	% AGE
NET LAND AREA	52086.00	100.00
COVERED AREA OF ONE FARM	78.50	0.151
131 X 78.50 SQM	10283.50	19.743
COVERED AREA OF MUMTY	9.71	0.019
131 X 16.22 SQM	1272.01	2.442
TOTAL COVERED AREA	11555.51	22.185
F. A.R.	10283.50	19.743

LEGEND :-

PROPOSED CONST.	
OTHER'S LAND	
DRAINAGE LINE	
ELECTRIC LINE	

PROPOSED PLAN FOR A FARM

HOUSE BUILDING ON KHASRA NO.-

583, 584, 585, 586, MAUZA - KONAI

AND KHASRA NO - 28, MAUZA -

JULHENDI, TEHSIL & DISTT.

MATHURA.

OWNER :-

M/S DIVIT LANDS PRIVATE LIMITED
AUTH. - SHRI SANTOSH SINGHAL
S/O SHRI RAM BABU

NORTH :-



APPLICANT SIGN.

Ar. Kanchana Agrawal
(M. Arch)
Reg. No. CA/2016/79875
Architect & Valuer

ENGI SIGN.

SCALE:-

1 : 100

DATE

DRG NO.